CARTE DE STATIONNEMENT ET D'ACCOSTAGE D'AERONEF - OACI -

ELEV AIRE DE TRAFIC 325 m

TWR 122.500

GUELMIME

ALTITUDES ET DIMENSIONS EN METRES
RELEVEMENTS MAGNETIQUES

COORDONNEES WGS84 DES POSTES DE STATIONNEMENT DES AERONEFS			ALT	FORCE PORTANTE
1	29° 01' 02.72" N	010° 03' 09.02" W	324.46	PCR 1060/F/B/X/T
2	29° 01' 03.63" N	010° 03' 07.23" W	324.74	
3	29° 01' 04.53" N	010° 03' 05.37" W	324.62	
4	29° 01' 05.43" N	010° 03' 03.54" W	324.35	
J	29° 01' 03.62" N	010° 03' 08.17" W	324.58	

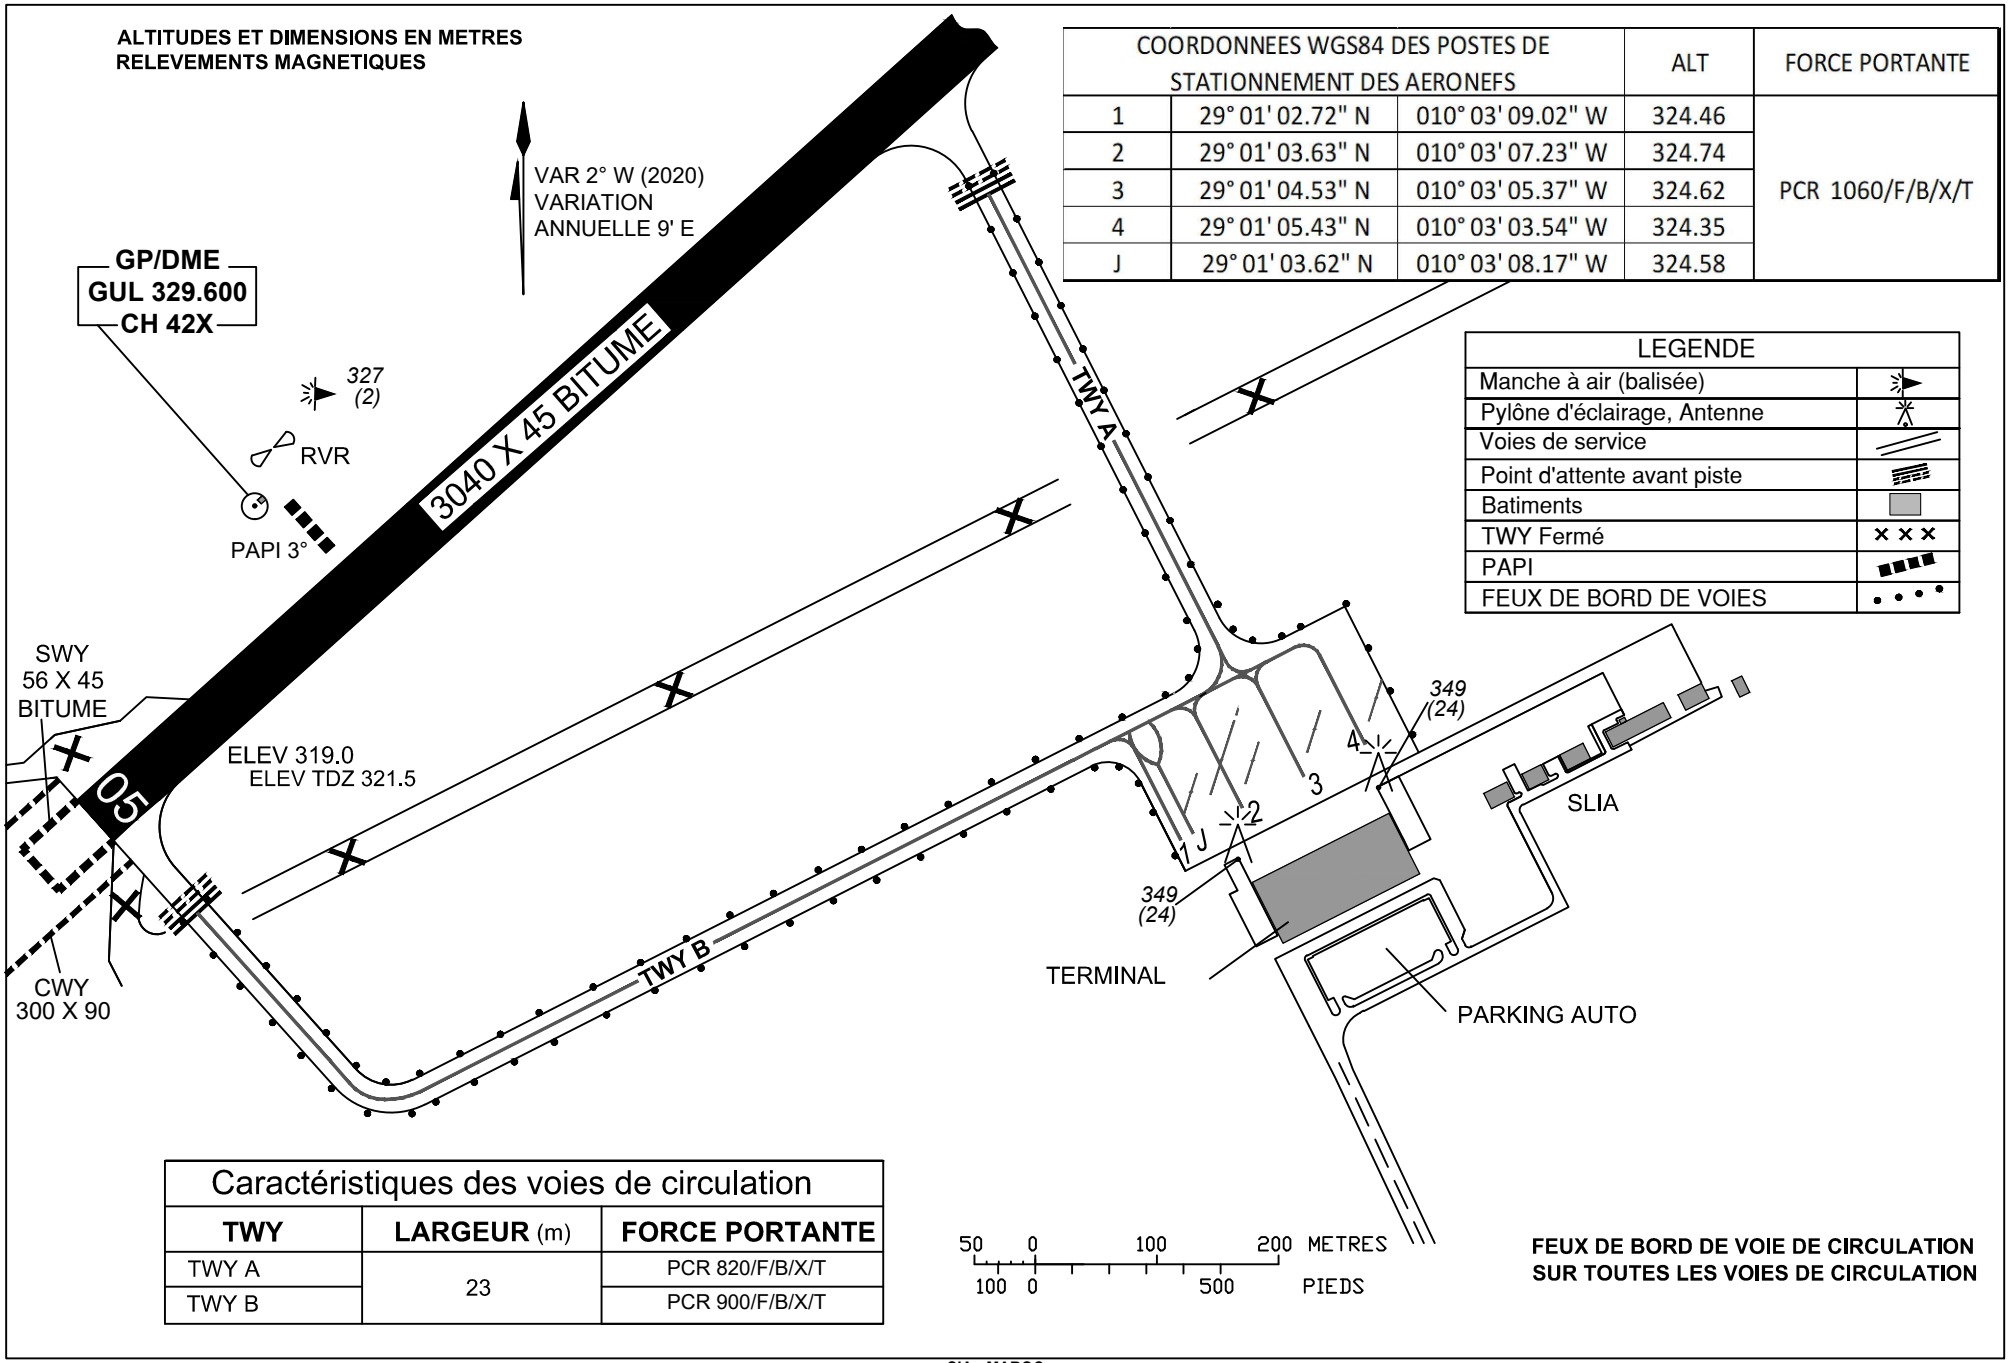

LEGENDE	
Manche à air (balisée)	
Pylône d'éclairage, Antenne	
Voies de service	
Point d'attente avant piste	
Batiments	
TWY Fermé	× × ×
PAPI	
FEUX DE BORD DE VOIES	

Caractéristiques des voies de circulation		
TWY	**LARGEUR** (m)	**FORCE PORTANTE**
TWY A	23	PCR 820/F/B/X/T
TWY B		PCR 900/F/B/X/T

FEUX DE BORD DE VOIE DE CIRCULATION SUR TOUTES LES VOIES DE CIRCULATION