BOUARFA

TWR 118.000

ELEV
AIRE DE TRAFIC
1117m

CARTE DE STATIONNEMENT
ET D'ACCOSTAGE
D'AERONEF-OACI

AIP
MAROC

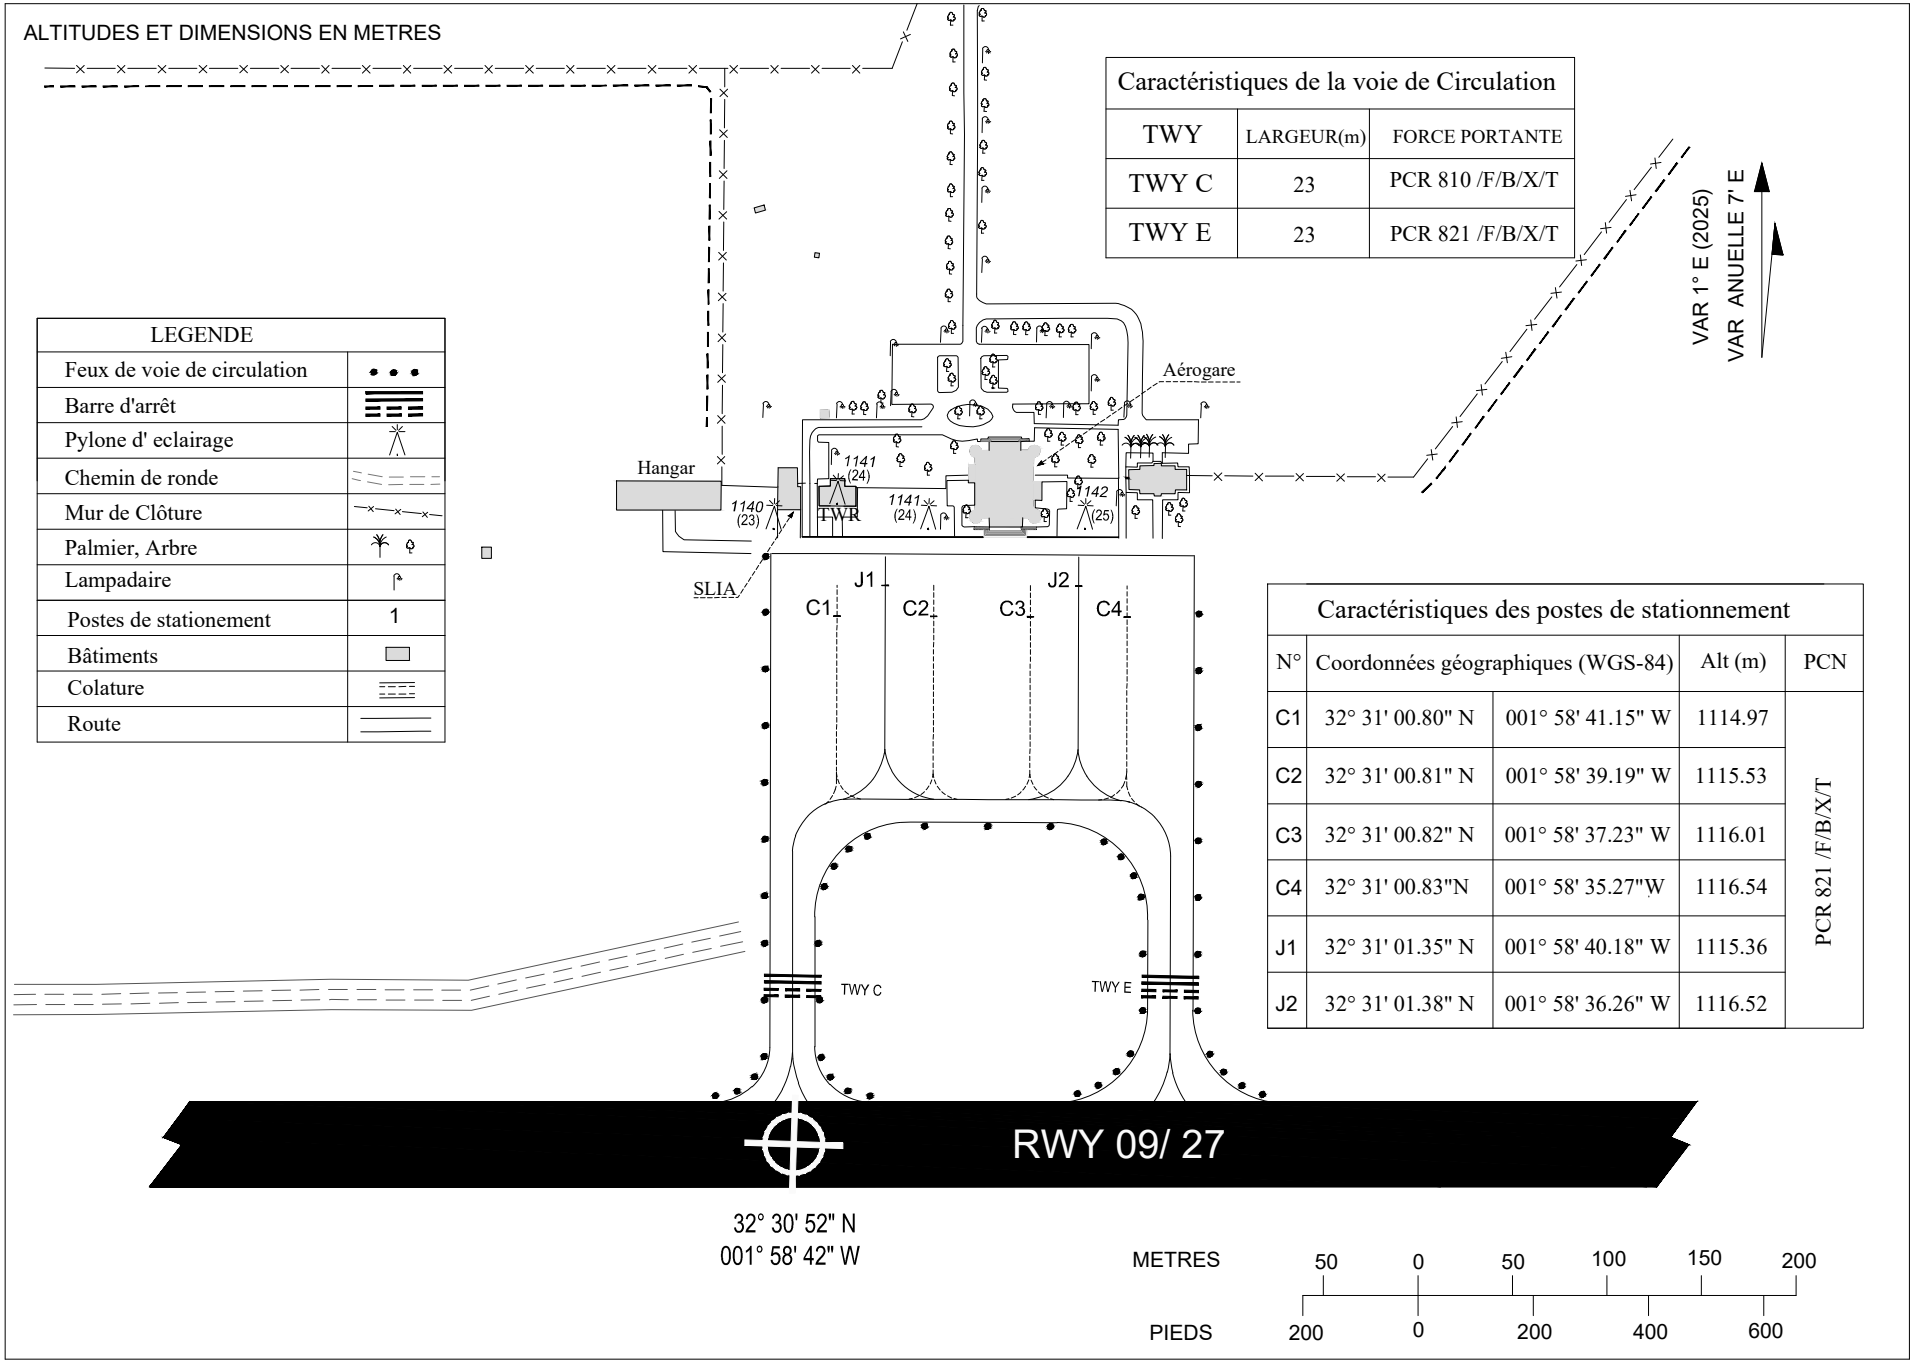

LEGENDE	
Feux de voie de circulation	
Barre d'arrêt	
Pylone d' eclairage	
Chemin de ronde	
Mur de Clôture	
Palmier, Arbre	
Lampadaire	
Postes de stationement	1
Bâtiments	
Colature	
Route	

Caractéristiques de la voie de Circulation		
TWY	LARGEUR(m)	FORCE PORTANTE
TWY C	23	PCR 810 /F/B/X/T
TWY E	23	PCR 821 /F/B/X/T

Caractéristiques des postes de stationnement				
N°	Coordonnées géographiques (WGS-84)		Alt (m)	PCN
C1	32° 31' 00.80" N	001° 58' 41.15" W	1114.97	PCR 821 /F/B/X/T
C2	32° 31' 00.81" N	001° 58' 39.19" W	1115.53	
C3	32° 31' 00.82" N	001° 58' 37.23" W	1116.01	
C4	32° 31' 00.83"N	001° 58' 35.27"W	1116.54	
J1	32° 31' 01.35" N	001° 58' 40.18" W	1115.36	
J2	32° 31' 01.38" N	001° 58' 36.26" W	1116.52	