CARTE DES MOUVEMENTS A LA SURFACE DE L'AERODROME -OACI-

ELEV
AIRE DE TRAFIC
469 m

TWR	118.200
APP	136.600
D-ATIS	121.600

OUJDA / Angads

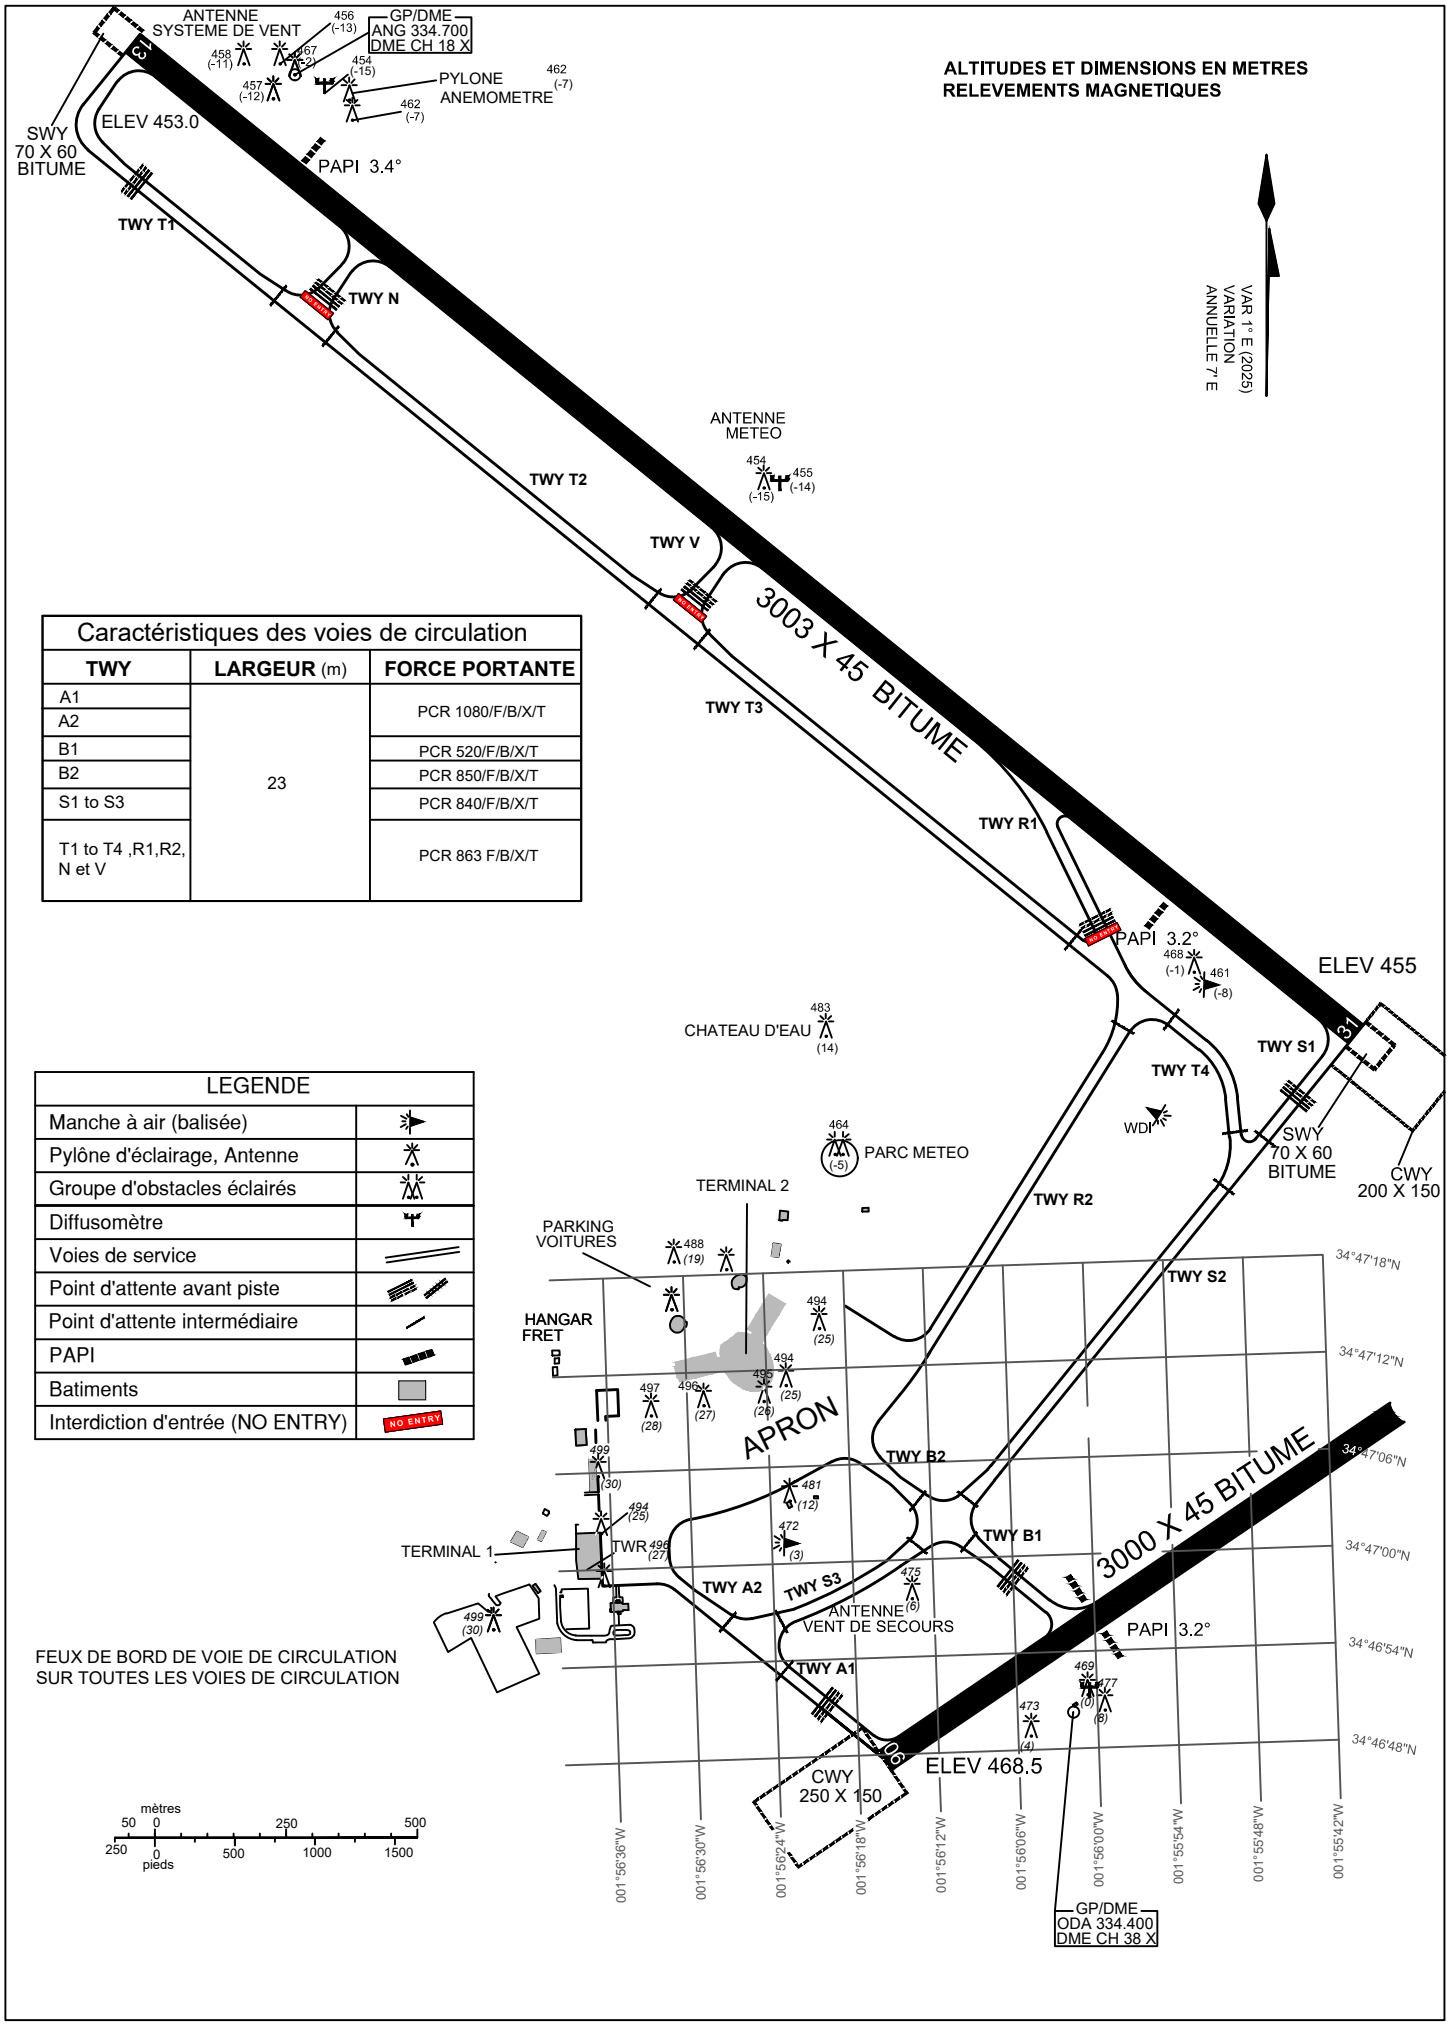

Caractéristiques des voies de circulation		
TWY	**LARGEUR** (m)	**FORCE PORTANTE**
A1	23	PCR 1080/F/B/X/T
A2		
B1		PCR 520/F/B/X/T
B2		PCR 850/F/B/X/T
S1 to S3		PCR 840/F/B/X/T
T1 to T4 ,R1,R2, N et V		PCR 863 F/B/X/T

LEGENDE	
Manche à air (balisée)	
Pylône d'éclairage, Antenne	
Groupe d'obstacles éclairés	
Diffusomètre	
Voies de service	
Point d'attente avant piste	
Point d'attente intermédiaire	
PAPI	
Batiments	
Interdiction d'entrée (NO ENTRY)	NO ENTRY

FEUX DE BORD DE VOIE DE CIRCULATION
SUR TOUTES LES VOIES DE CIRCULATION