CARTE DES MOUVEMENTS A LA SURFACE DE L'AERODROME - OACI -

ELEV AIRE DE TRAFIC 196 m

TWR 129.700

TAN-TAN / Plage Blanche

ALTITUDES ET DIMENSIONS EN METRES
RELEVEMENTS MAGNETIQUES

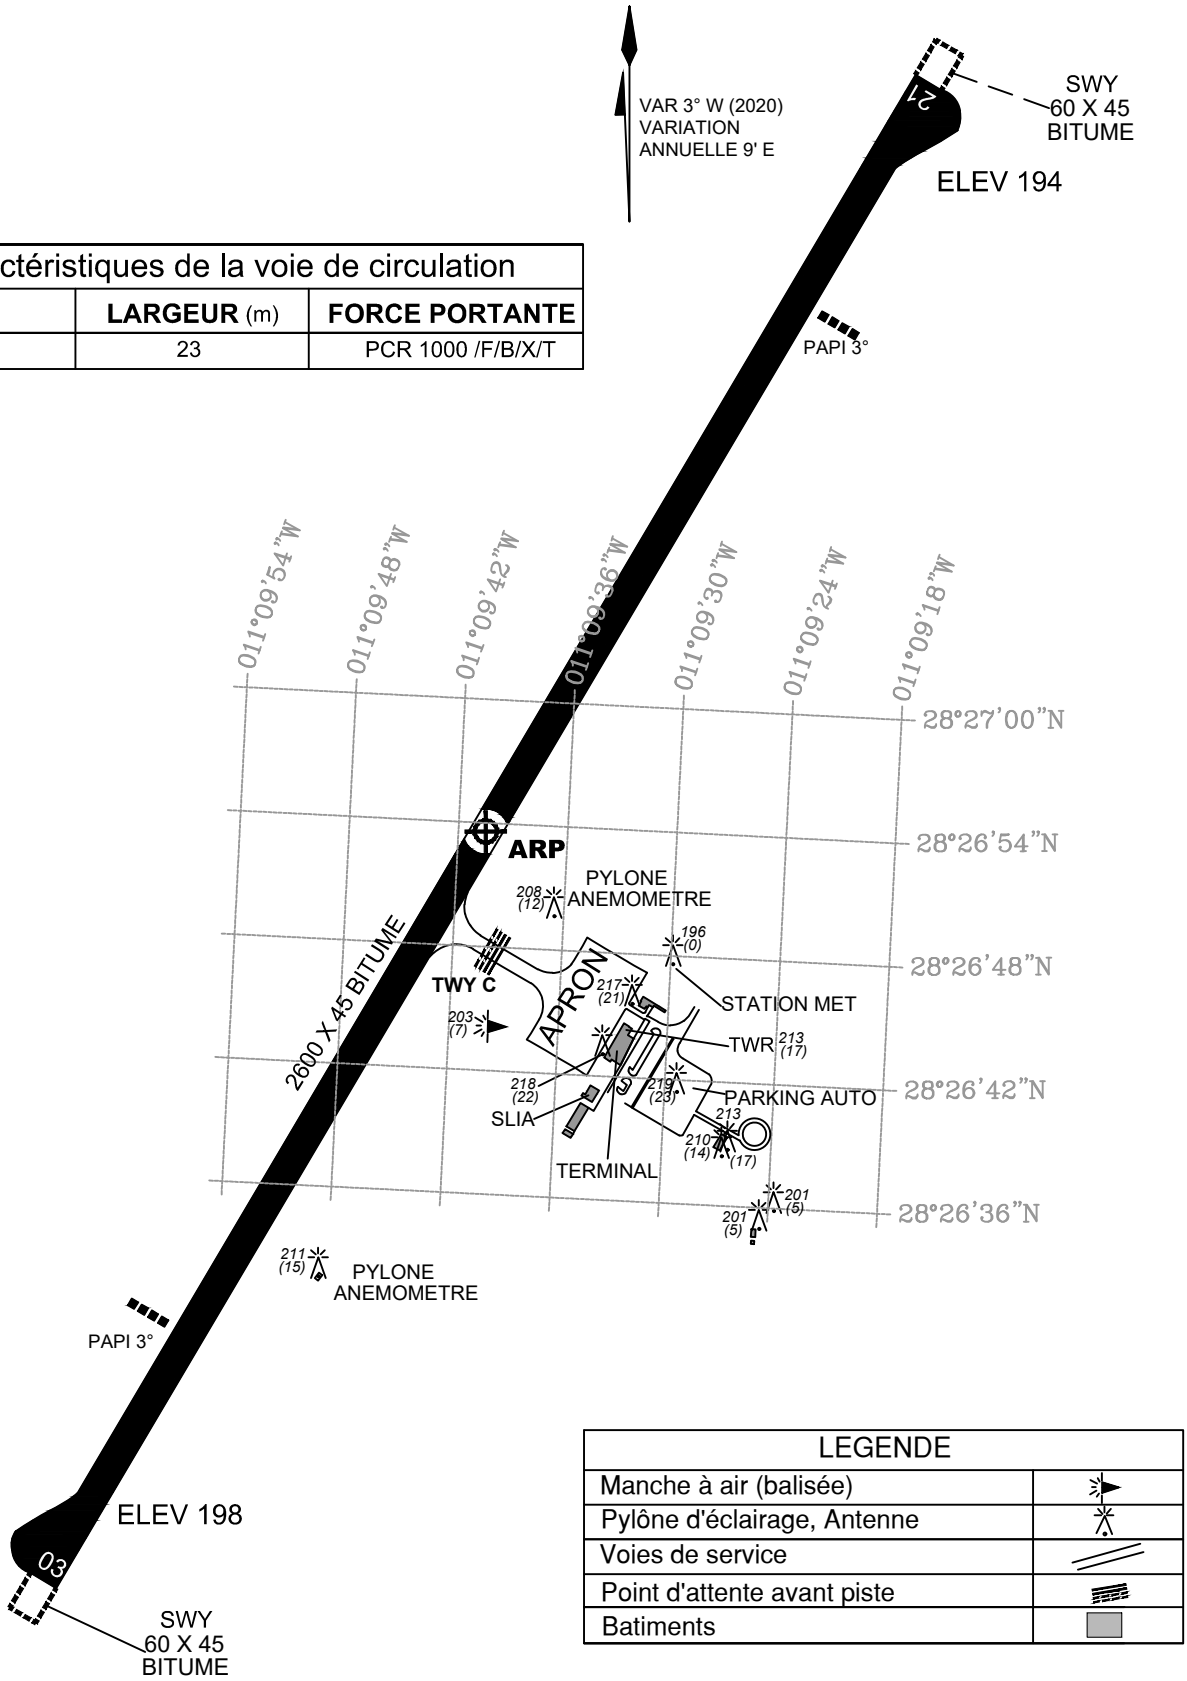

Caractéristiques de la voie de circulation		
TWY	**LARGEUR** (m)	**FORCE PORTANTE**
TWY C	23	PCR 1000 /F/B/X/T

LEGENDE	
Manche à air (balisée)	
Pylône d'éclairage, Antenne	
Voies de service	
Point d'attente avant piste	
Batiments	

FEUX DE BORD DE VOIE DE CIRCULATION SUR TOUTES LES VOIES DE CIRCULATION