CARTE DES MOUVEMENTS
A LA SURFACE DE L'AERODROME -OACI-

ELEV
AIRE DE TRAFIC
1661m

TWR 131.000

IFRANE

ALTITUDES ET DIMENSIONS EN METRES
RELEVEMENTS MAGNETIQUES

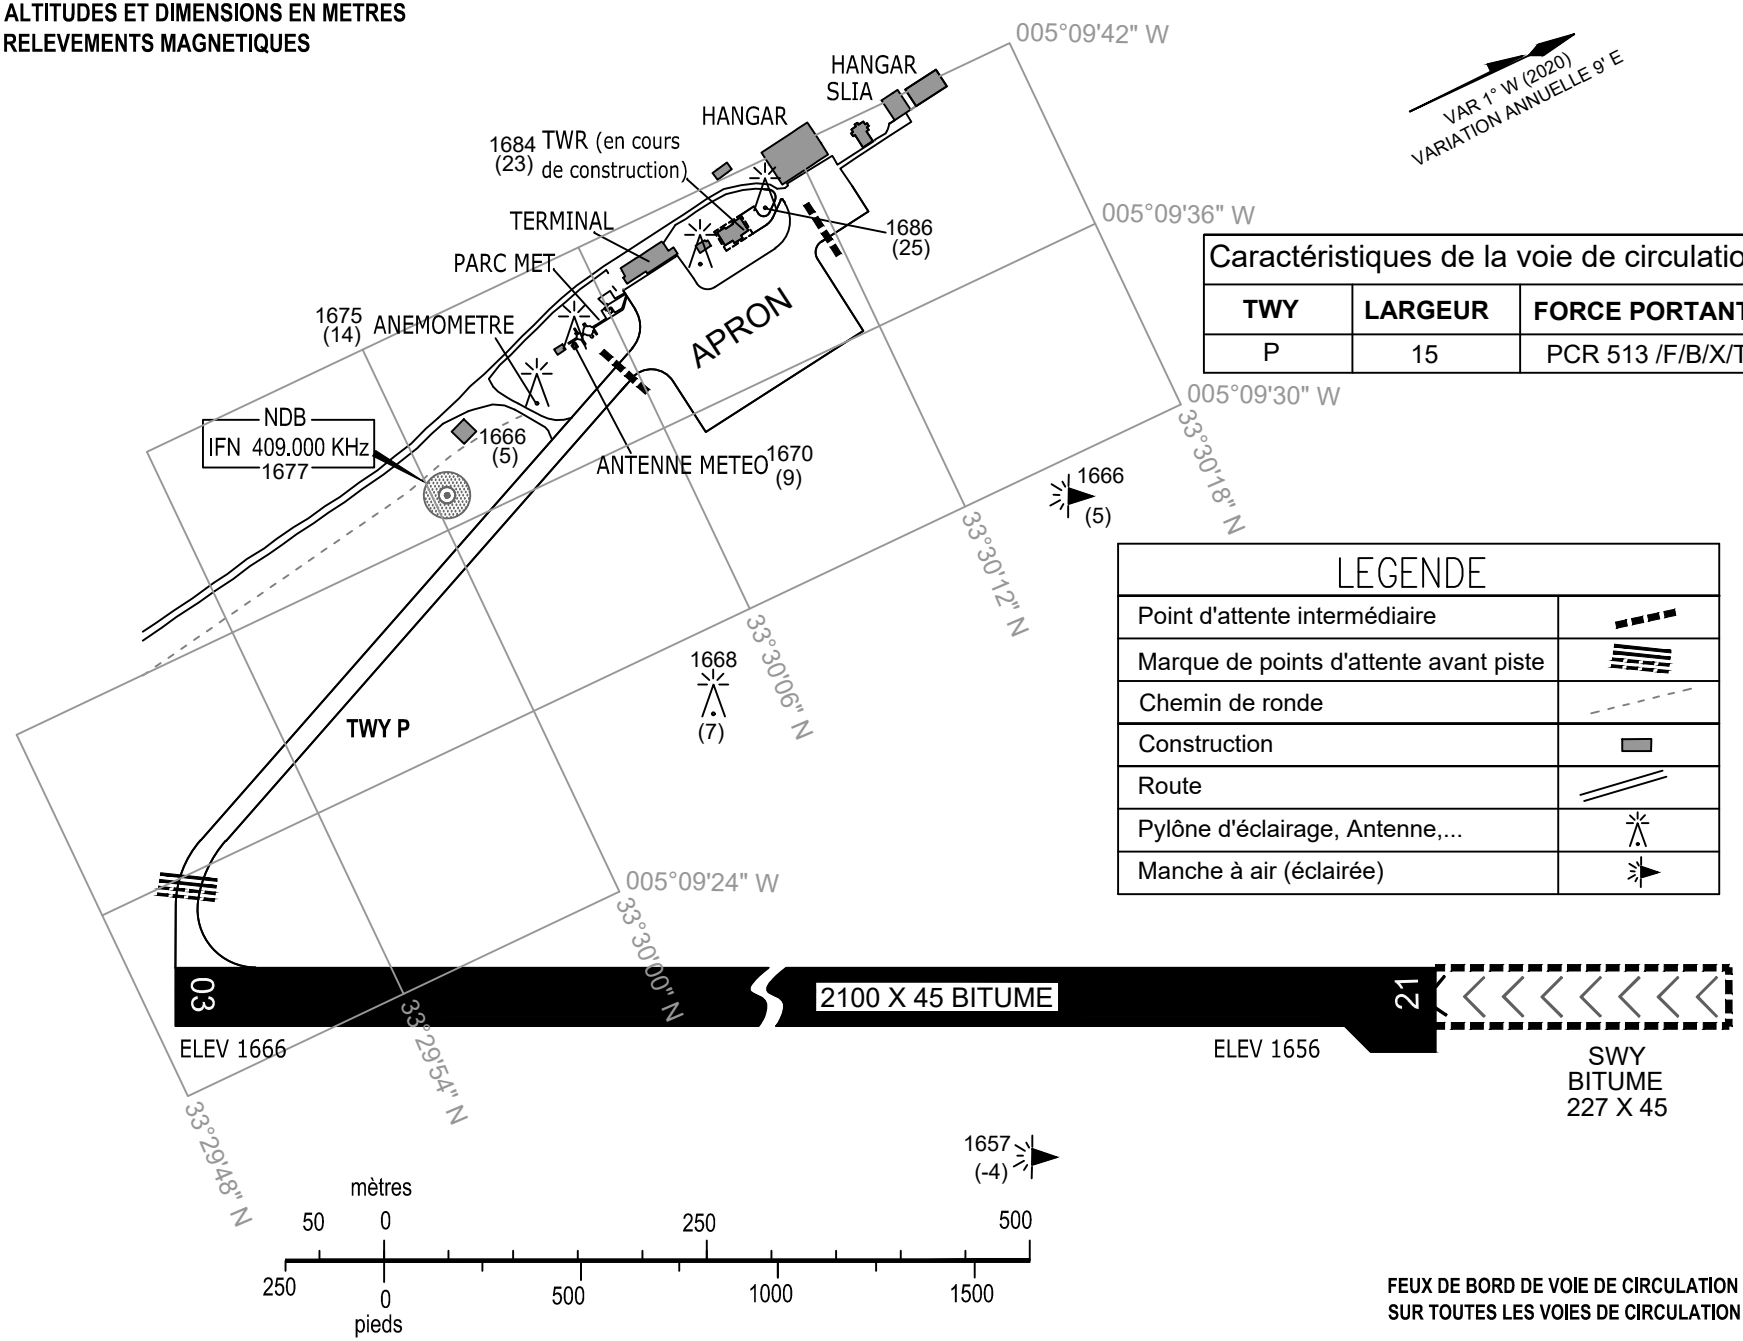

Caractéristiques de la voie de circulation		
TWY	**LARGEUR**	**FORCE PORTANTE**
P	15	PCR 513 /F/B/X/T

LEGENDE	
Point d'attente intermédiaire	
Marque de points d'attente avant piste	
Chemin de ronde	
Construction	
Route	
Pylône d'éclairage, Antenne,...	
Manche à air (éclairée)	

FEUX DE BORD DE VOIE DE CIRCULATION
SUR TOUTES LES VOIES DE CIRCULATION