CARTE DE STATIONNEMENT ET D'ACCOSTAGE D'AERONEF -OACI-

ELEV
AIRE DE TRAFIC
469 m

TWR 118.200

OUJDA / Angads

Caractéristiques des voies de circulation		
TWY	**LARGEUR** (m)	**FORCE PORTANTE**
A1	23	PCR 1080/F/B/X/T
A2		
B1		PCR 520/F/B/X/T
B2		PCR 850/F/B/X/T
S1 to S3		PCR 840/F/B/X/T
T1 to T4 ,R1,R2, N et V		PCR 863 F/B/X/T

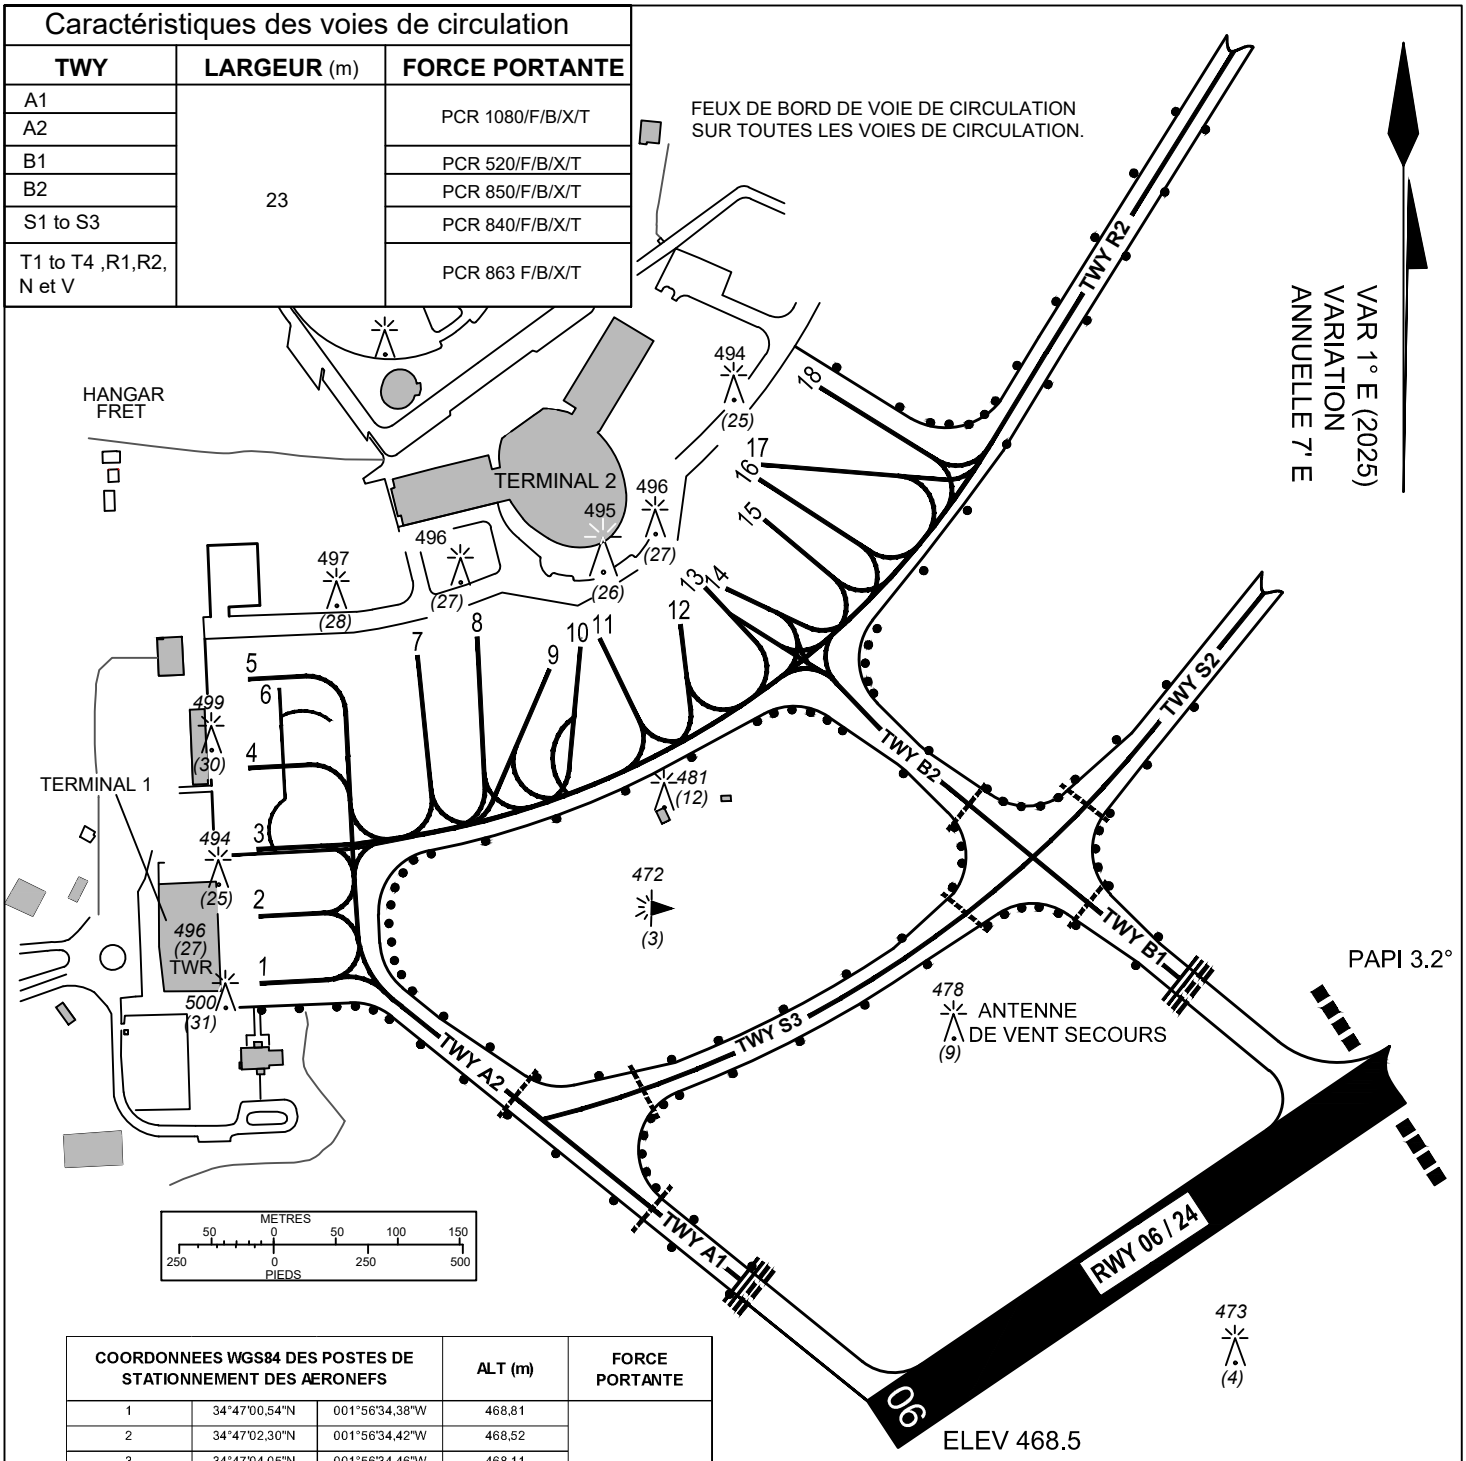

COORDONNEES WGS84 DES POSTES DE STATIONNEMENT DES AERONEFS			ALT (m)	FORCE PORTANTE
1	34°47'00,54"N	001°56'34,38"W	468,81	PCR 863/F/B/X/T
2	34°47'02,30"N	001°56'34,42"W	468,52	
3	34°47'04,05"N	001°56'34,46"W	468,11	
4	34°47'06,72"N	001°56'33,72"W	467,35	
5	34°47'08,29"N	001°56'34,96"W	467,15	
6	34°47'06,63"N	001°56'34,55"W	467,49	
7	34°47'08,64"N	001°56'30,36"W	466,06	PCR 1090/R/B/W/T
8	34°47'09,13"N	001°56'28,42"W	465,35	
9	34°47'08,11"N	001°56'25,92"W	465,15	
10	34°47'08,70"N	001°56'25,08"W	464,94	
11	34°47'08,84"N	001°56'24,73"W	464,99	
12	34°47'08,74"N	001°56'21,95"W	464,69	
13	34°47'10,07"N	001°56'21,53"W	464,55	
14	34°47'09,99"N	001°56'21,25"W	464,53	
15	34°47'11,82"N	001°56'19,73"W	464,37	
16	34°47'12,84"N	001°56'19,93"W	464,5	
17	34°47'12,93"N	001°56'19,98"W	464,51	
18	34°47'15,09"N	001°56'17,76"W	463,68	

LEGENDE	
Poste de Stationnnement	7
Manche à air (balisée)	
Pylône d'éclairage, Antenne	
Chemin de ronde	
Voies de service	
Point d'attente avant piste	
Point d'attente intermédiaire	
PAPI	
Batiments	
Feux de balisage lumineux	