CARTE D'AERODROME/
D'HELISTATION -OACI

ARP
32°24'07"N
006°18'58"W

ELEV 518 m

TWR 121.200

BENI MELLAL

ALTITUDE ET DIMENTION EN METRES
RELEVEMENTS MAGNETIQUES

RWY	DIRECTION	THR	FORCES PORTANTES	
05	047°	32°23'38"N 006°19'32"W	Du 0m à 1200m Du 1200m à 2490m	PCR 740/F/C/X/T PCR 610/F/B/X/T
23	227°	32°24'35"N 006°18'24"W	Du 0m à 1290m Du 1290m à 2490m	PCR 610/F/B/X/T PCR 740/F/C/X/T

CARACTERISTIQUES DE LA VOIE DE CIRCULATION		
TWY	LARGEUR (m)	FORCE PORTANTE
TWY C	23	PCR 740/F/C/X/T
TWY L	08	5700 Kg/0,90 MPA
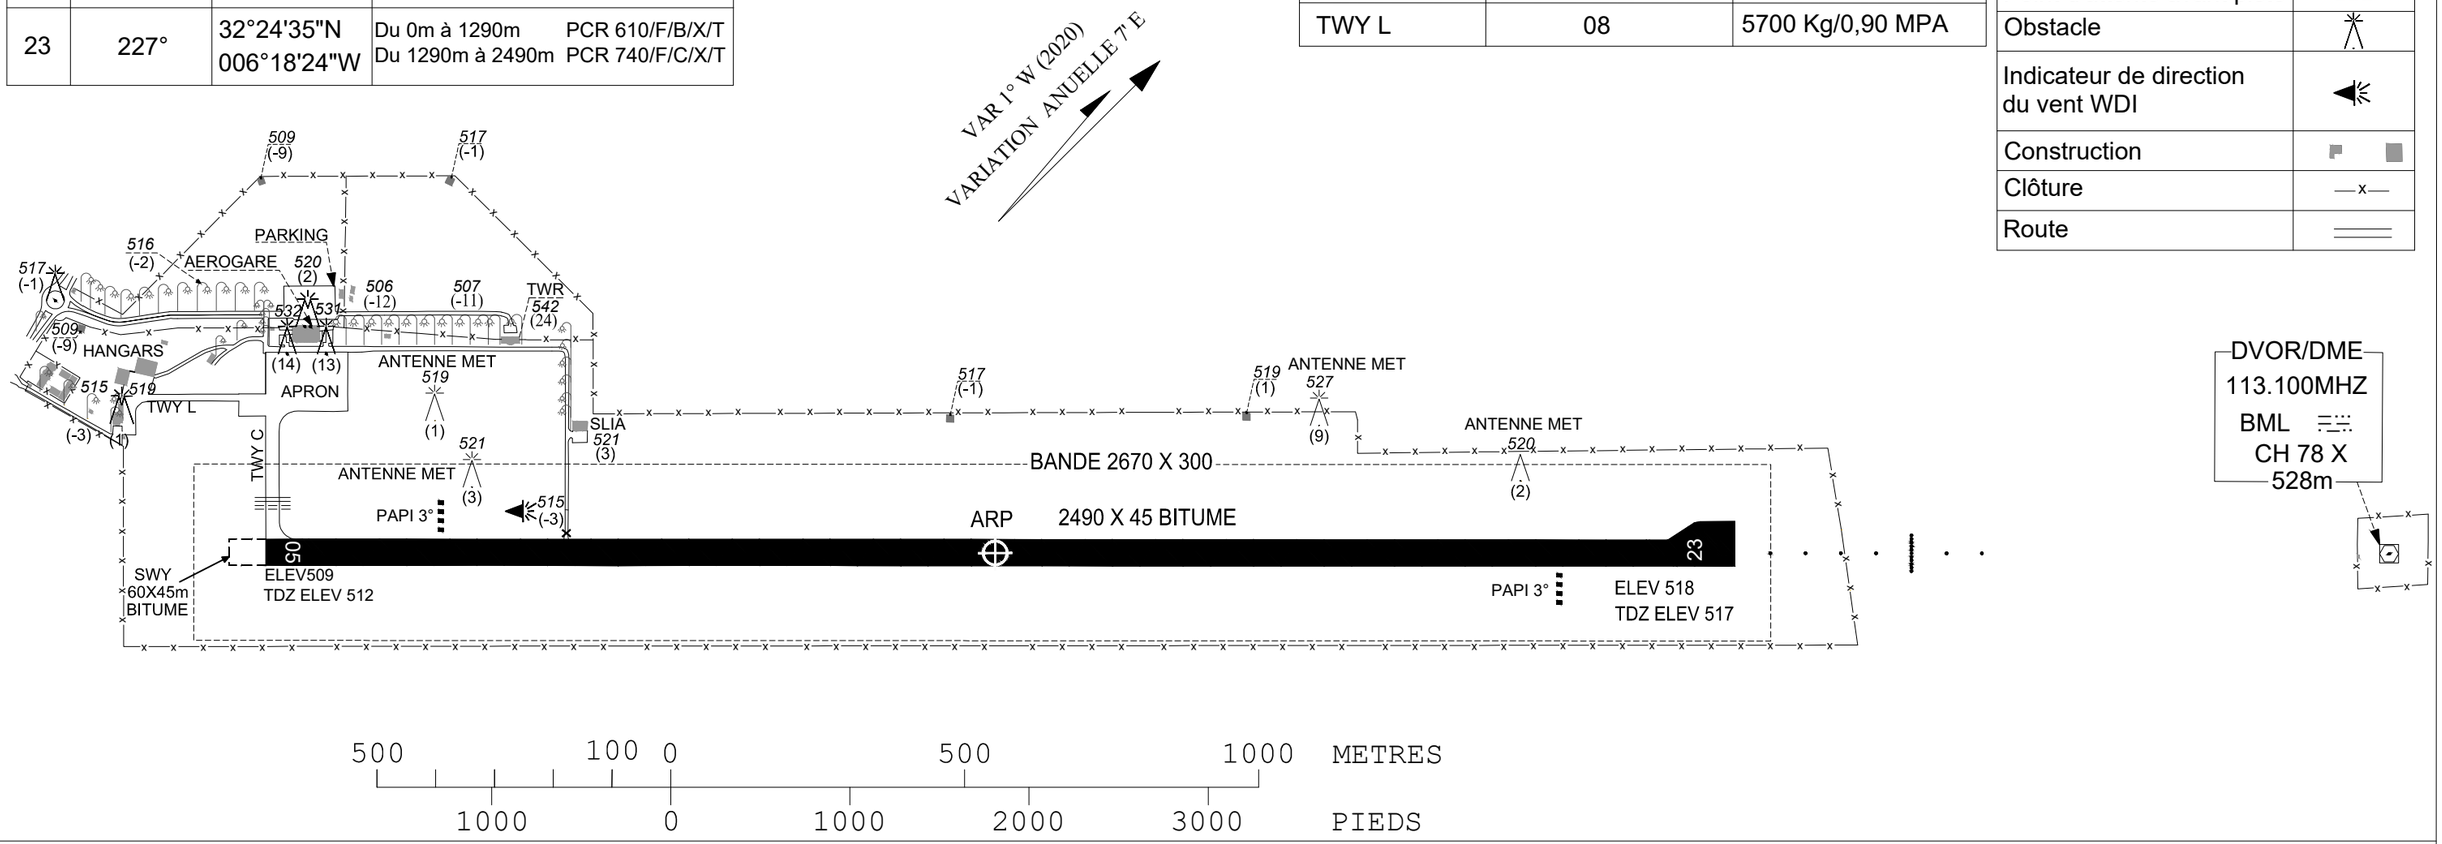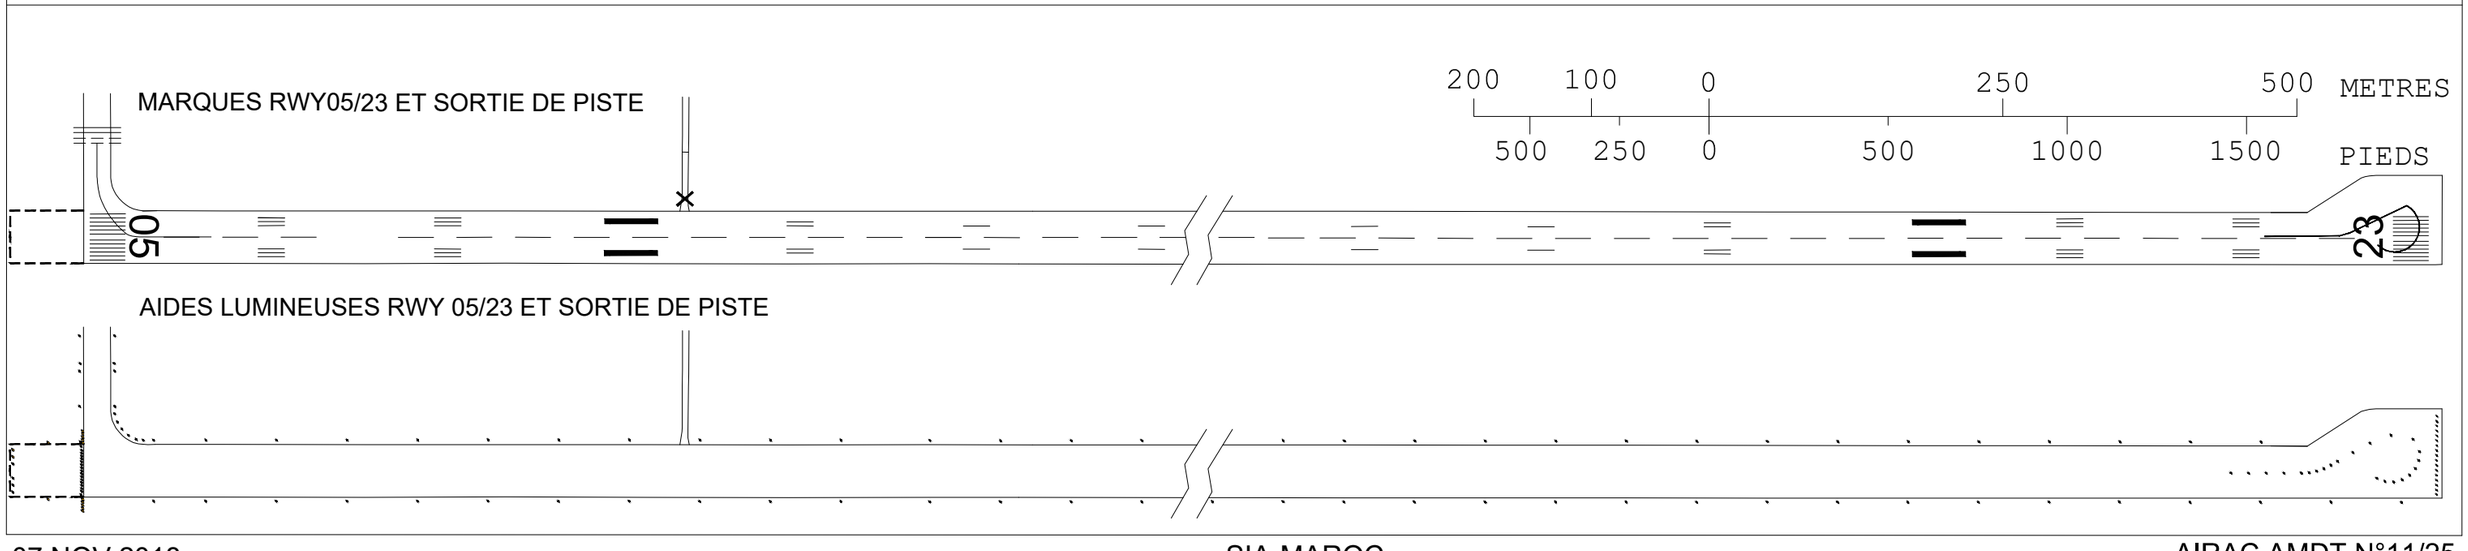
LEGENDE	
Lampadaire	
Point d'attente avant piste	
Obstacle	
Indicateur de direction du vent WDI	
Construction	
Clôture	
Route