CARTE DE STATIONNEMENT ET D'ACCOSTAGE D'AERONEF - OACI -

ELEV AIRE DE TRAFIC 8 m

TWR 118.100

DAKHLA

ALTITUDES ET DIMENSIONS EN METRES

FEUX DE BORD DE VOIE DE CIRCULATION SUR TOUTES LES VOIES DE CIRCULATION

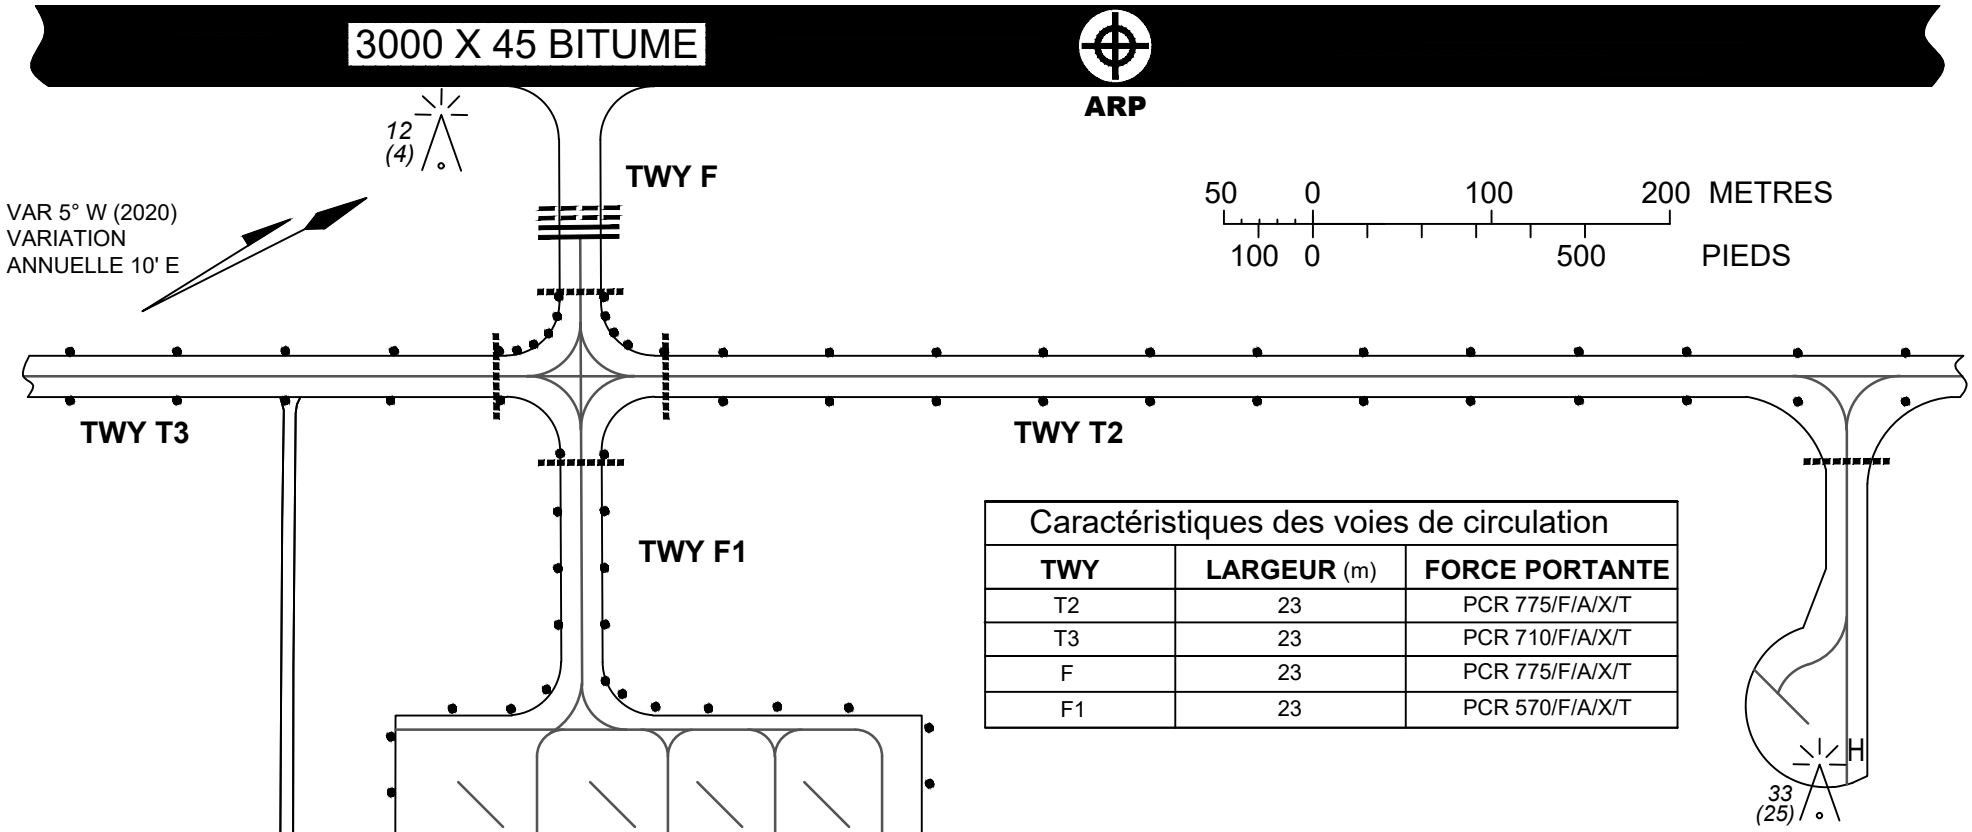

Caractéristiques des voies de circulation		
TWY	**LARGEUR** (m)	**FORCE PORTANTE**
T2	23	PCR 775/F/A/X/T
T3	23	PCR 710/F/A/X/T
F	23	PCR 775/F/A/X/T
F1	23	PCR 570/F/A/X/T

COORDONNEES WGS84 DES POSTES DE STATIONNEMENT DES AERONEFS			**ALT (m)**	**FORCE PORTANTE**
A1	23°42'50,26"N	015°55'45,99"W	8,48	PCR 775/F/A/X/T
A2	23°42'52,48"N	015°55'44,98"W	8,36	PCR 510/F/A/X/T
A3	23°42'54,27"N	015°55'44,16"W	8,23	PCR 560/F/A/X/T
A4	23°42'56,07"N	015°55'43,34"W	7,91	PCR 775/F/A/X/T
POSTE ISOLE H	23°43'13,05"N	015°55'37,49"W	7,15	PCR 775/F/A/X/T

LEGENDE	
Feu de voie de circulation	
Pylône d'éclairage, Antenne	
Voies de service	
Point d'attente avant piste	
Point d'attente intermédiaire	
Batiments	