CARTE DES MOUVEMENTS A LA SURFACE DE L'AERODROME - OACI -

ELEV
AIRE DE TRAFIC
8 m

TWR	118.100
APP	119.500

DAKHLA

ALTITUDES ET DIMENSIONS EN METRES
RELEVEMENTS MAGNETIQUES

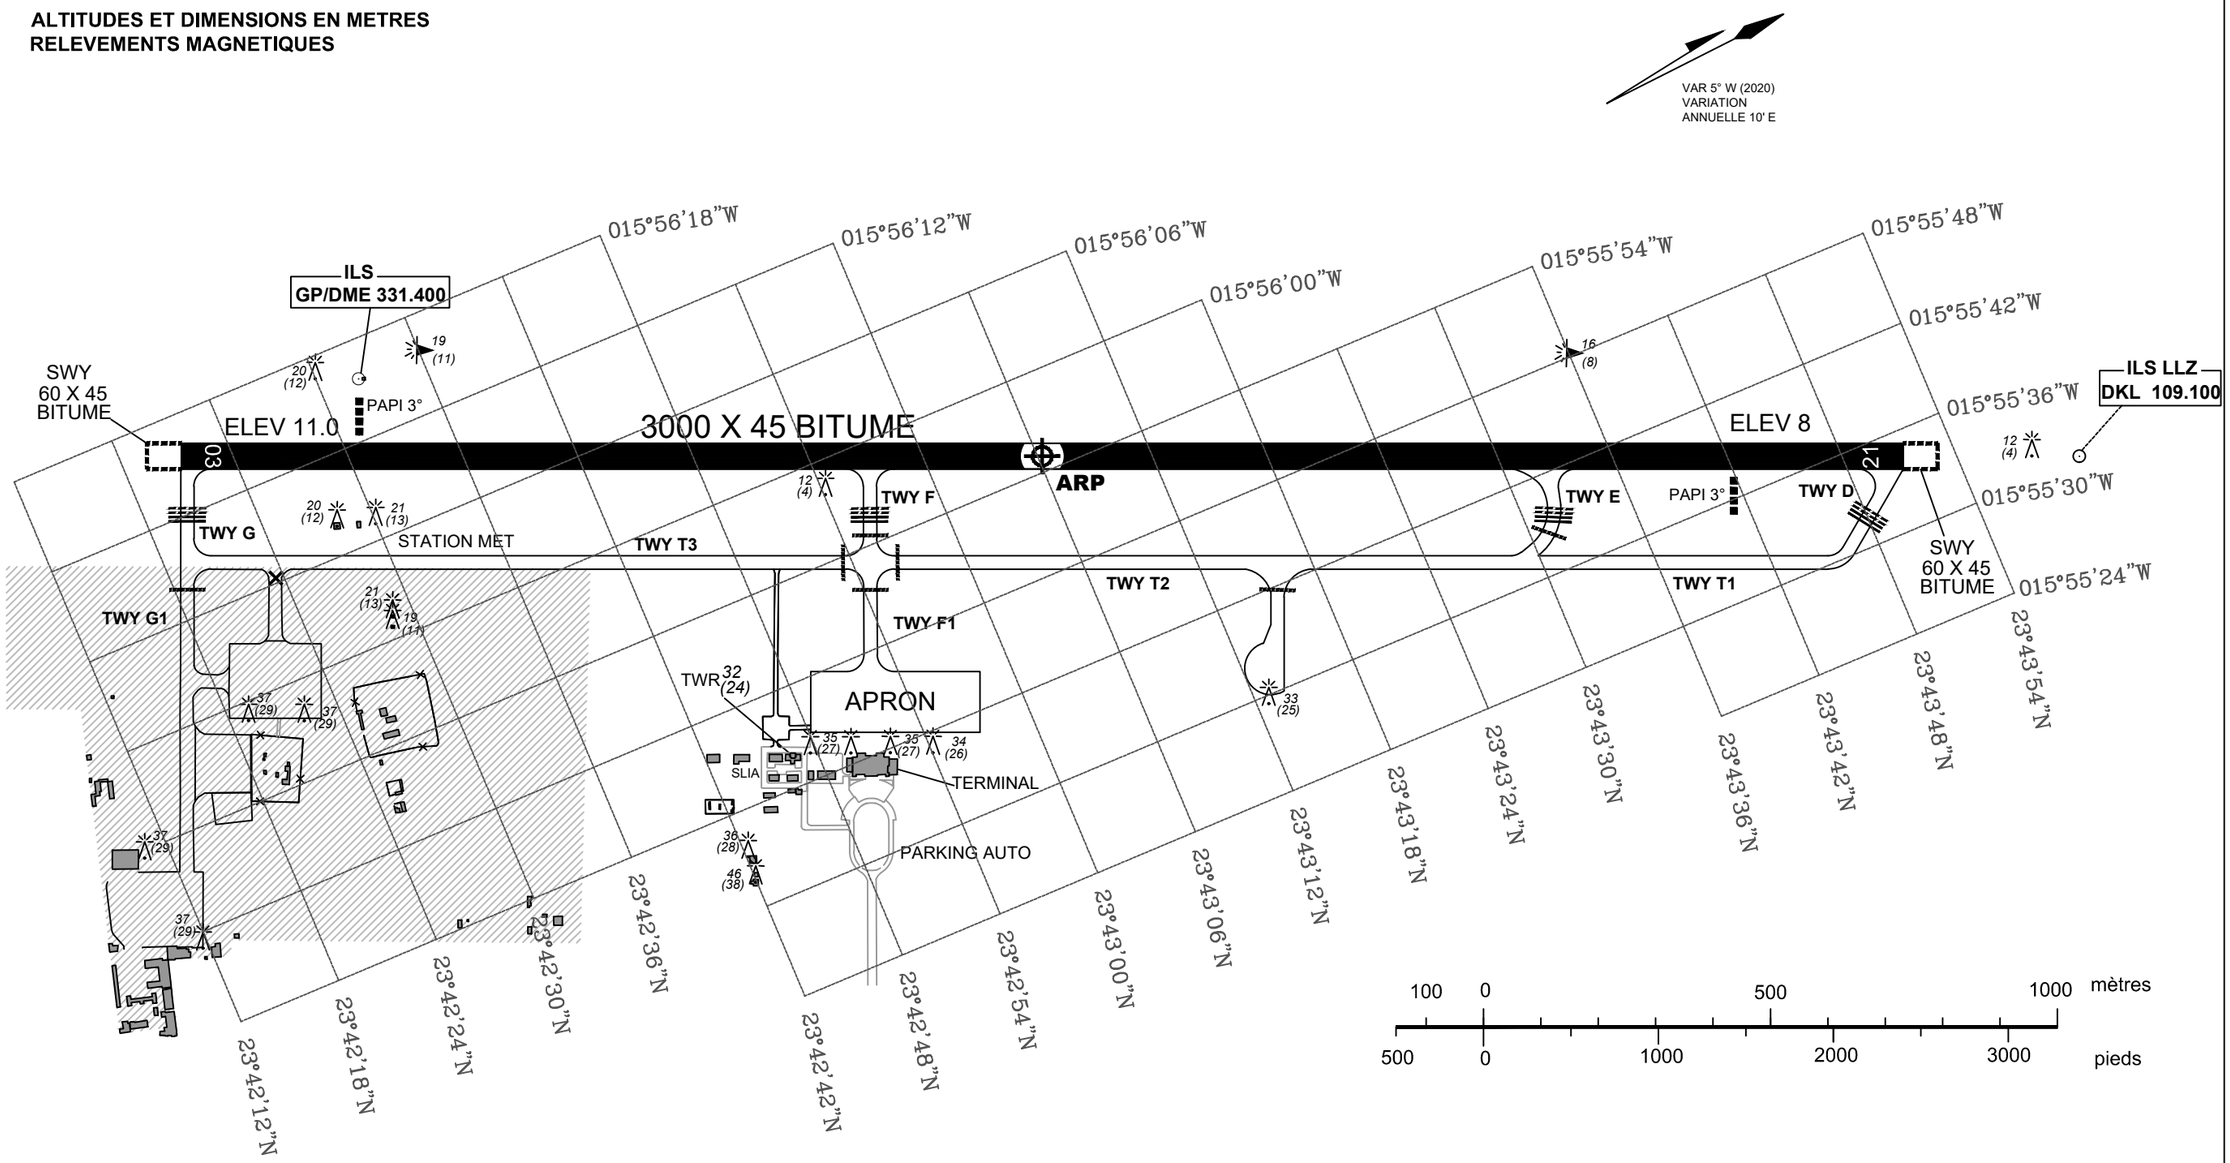

LEGENDE	
Manche à air (balisée)	
Pylône d'éclairage, Antenne	
Voies de service	
Point d'attente avant piste	
Point d'attente intermédiaire	
Batiments	
Zone militaire	
TWY Fermé	×

FEUX DE BORD DE VOIE DE CIRCULATION
SUR TOUTES LES VOIES DE CIRCULATION

Caractéristiques des voies de circulation

TWY	LARGEUR (m)	FORCE PORTANTE
T1	23	PCR 775/F/A/X/T
T2		
F		
G1		
D		
T3		PCR 710/F/A/X/T
E		PCR 500/F/A/X/T
F1		PCR 570/F/A/X/T
G		PCR 750/F/A/X/T